




Фасад в осях 1-9 М1:100

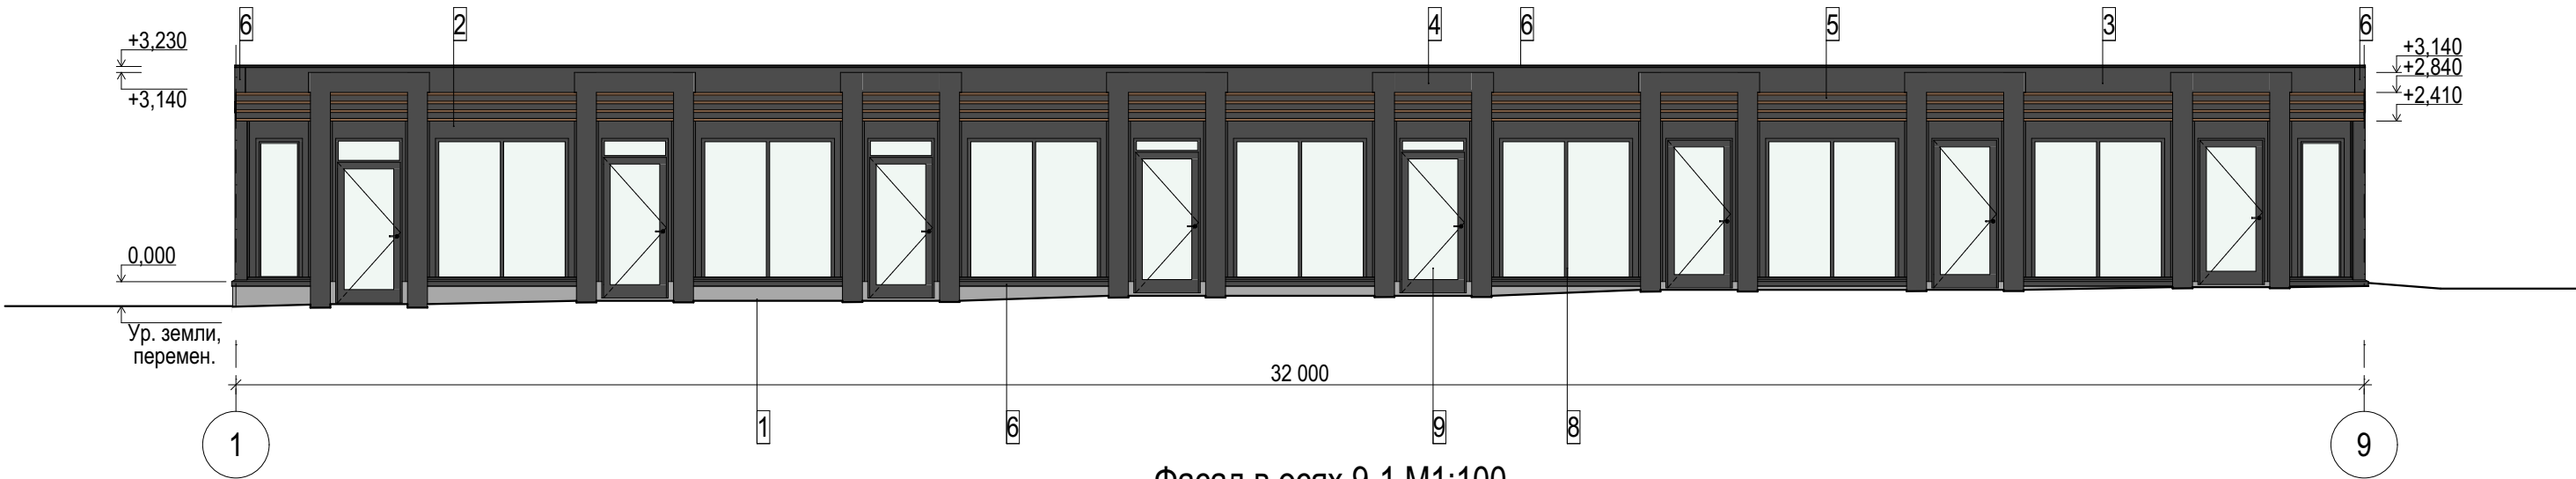


Фасад в осях 9-1 М1:100

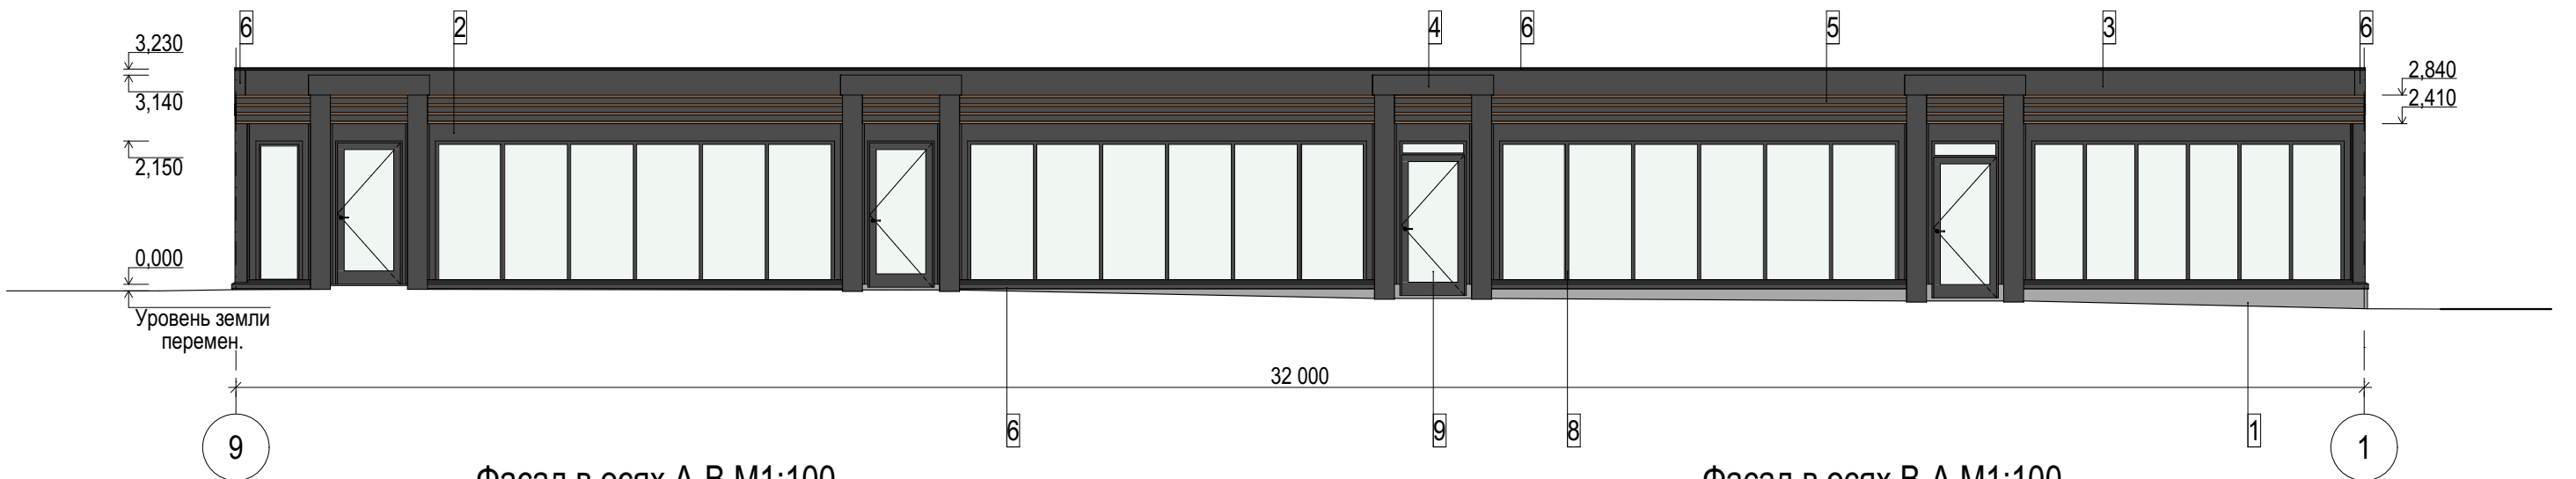

Фасад в осях А-В М1:100

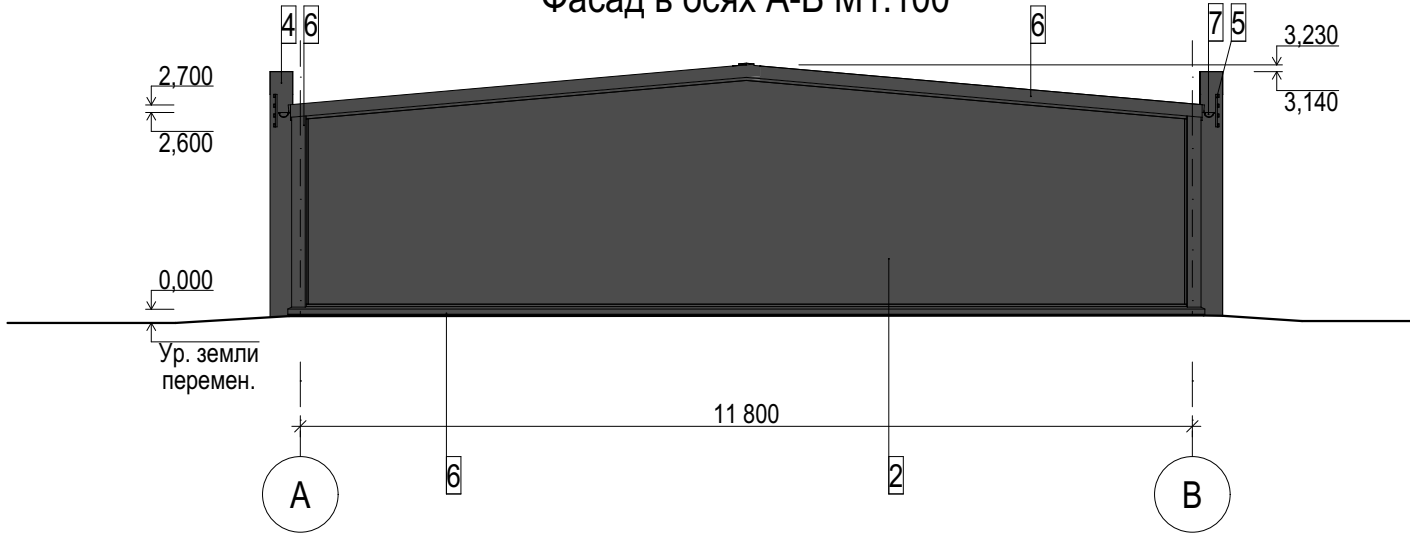

Фасад в осях В-А М1:100

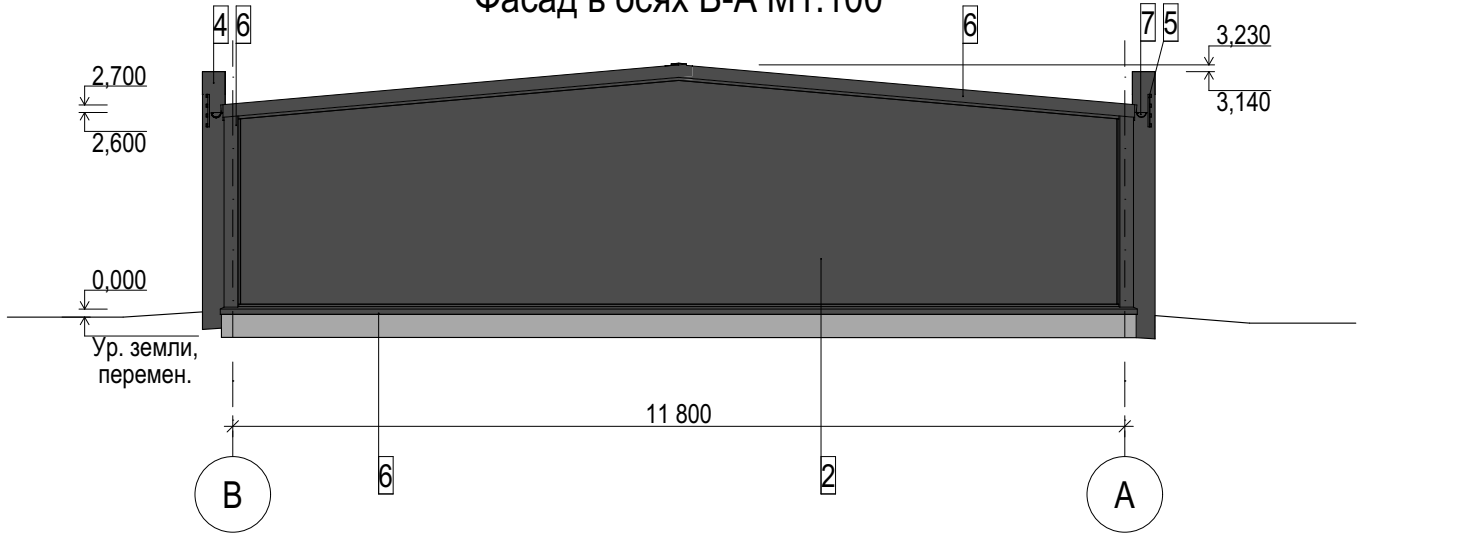

Примечания
1.Ведомость отделки фасадов см. лист 7
2.Все работы по отделке фасадов выполнять после завершения общестроительных работ.
3.Объемы в ведомости отделки даны в чистоте. Для заказа листовых материалов учитывать нахлест листов в соответствии с рекомендациями производителя.
4.Спецификации элементов заполнения проёмов см. лист 7
5. Стеновые сэндвич-панели толщиной 100мм, шириной 1190мм.
6. Кровельные сэндвич-панели толщиной 100мм, шириной 1140мм.

						868-25-AP			
						г. Брест, площадка по ул. Гвардейской в границах зданий 1 и 5			
Изм.	Коп.уч.	Лист	№Док.	Подп.	Дата	Открытая площадка с покрытием, расположенная в г. Бресте, в районе остановочного пункта общественного транспорта «Защитников Отечества» (четная сторона)	Стадия	Лист	Листов
							С	06	18
Разраб.	Горбач						Цветовое решение фасадов М1:100	ООО “АльденаГрупп”	
Проверил	Покалюк								
Н.контр.	Покалюк								