



Согласовано		Взам. инв. №	Подп. и дата	Инв. № подл.

Разрез 1 - 1

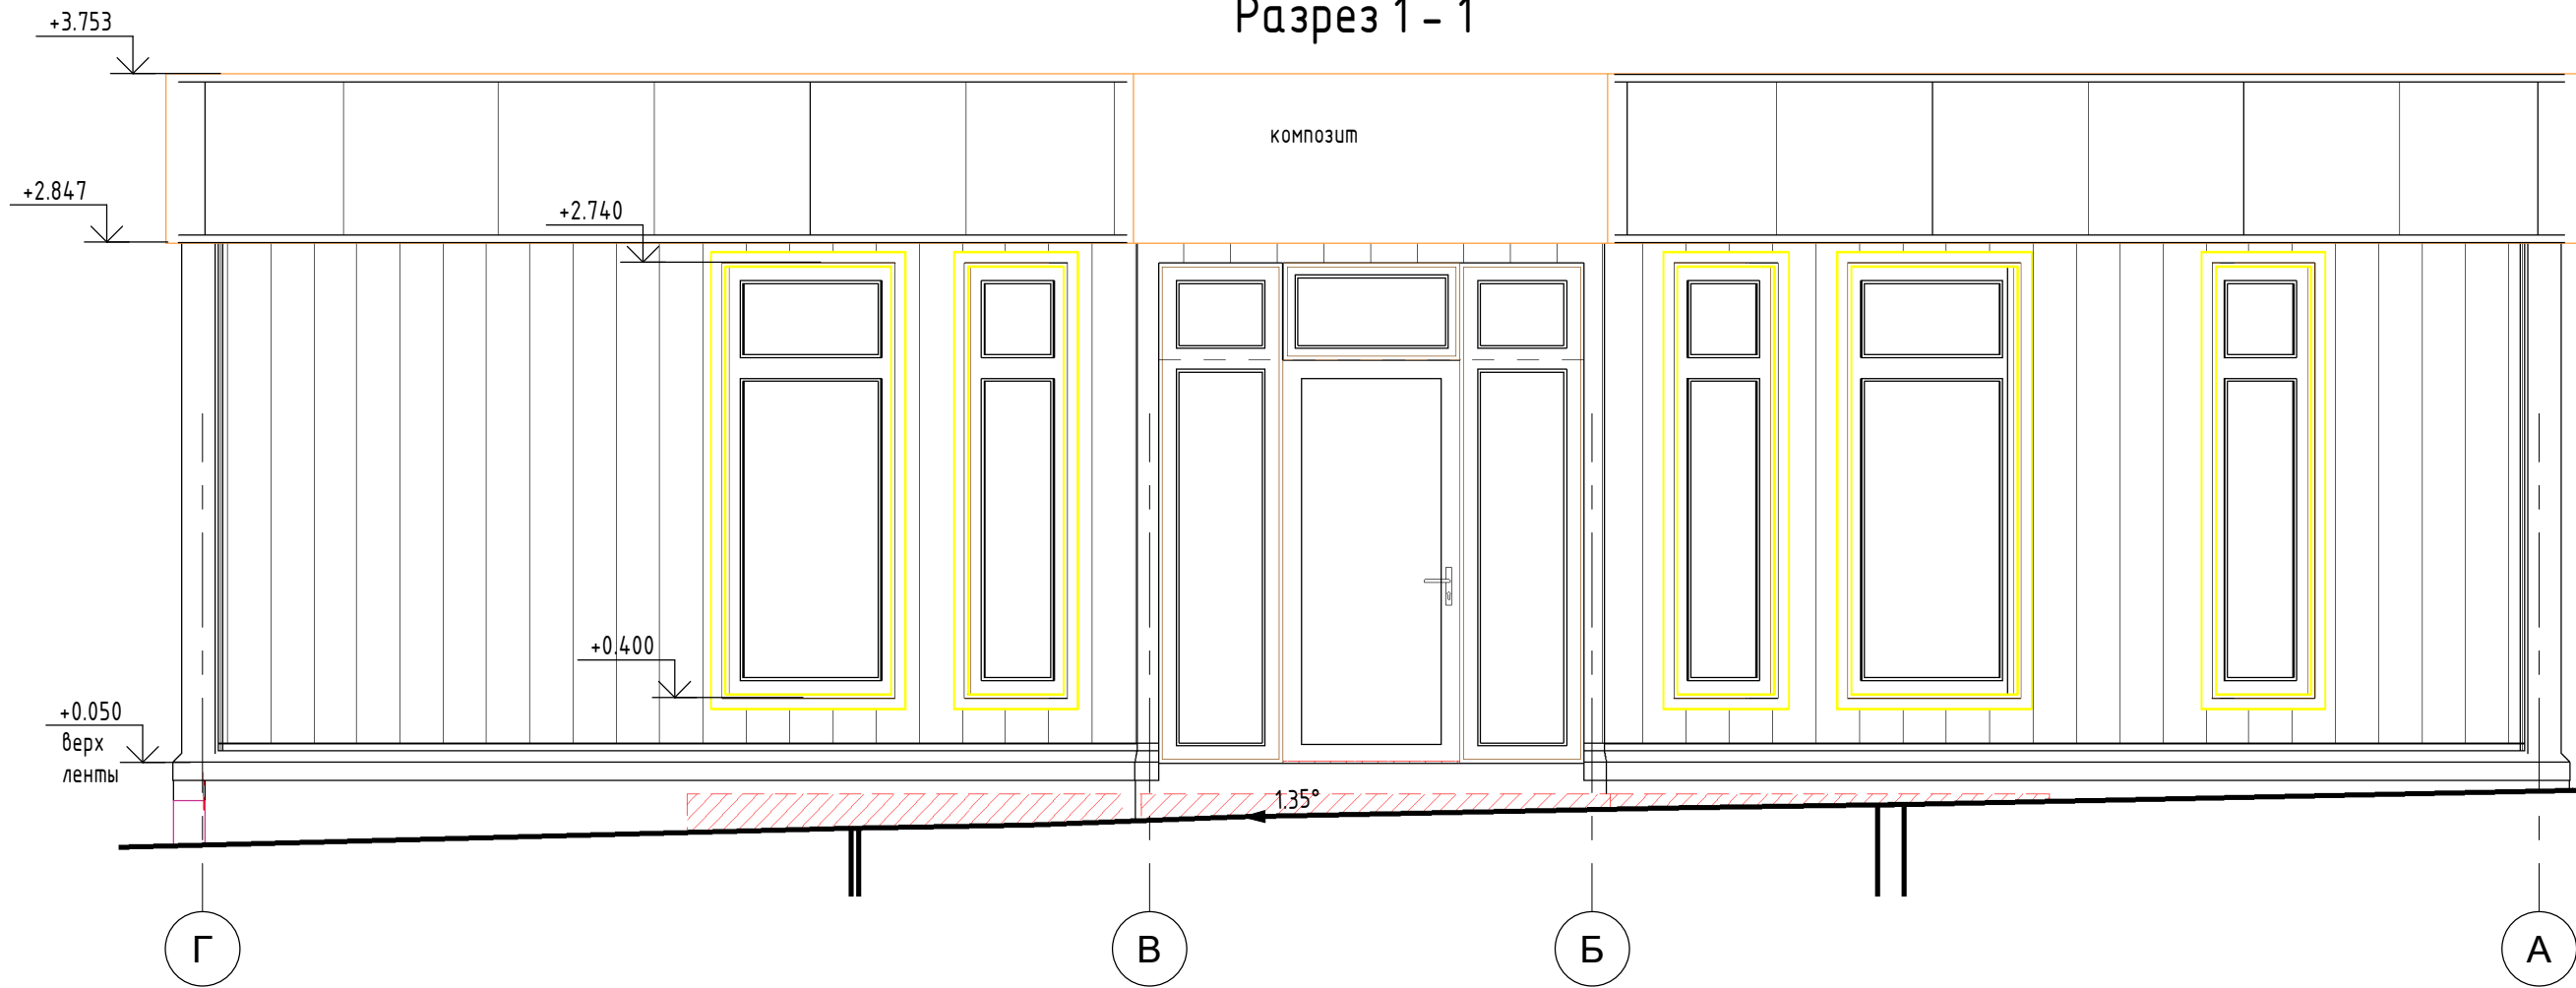


Разрез 4 - 4

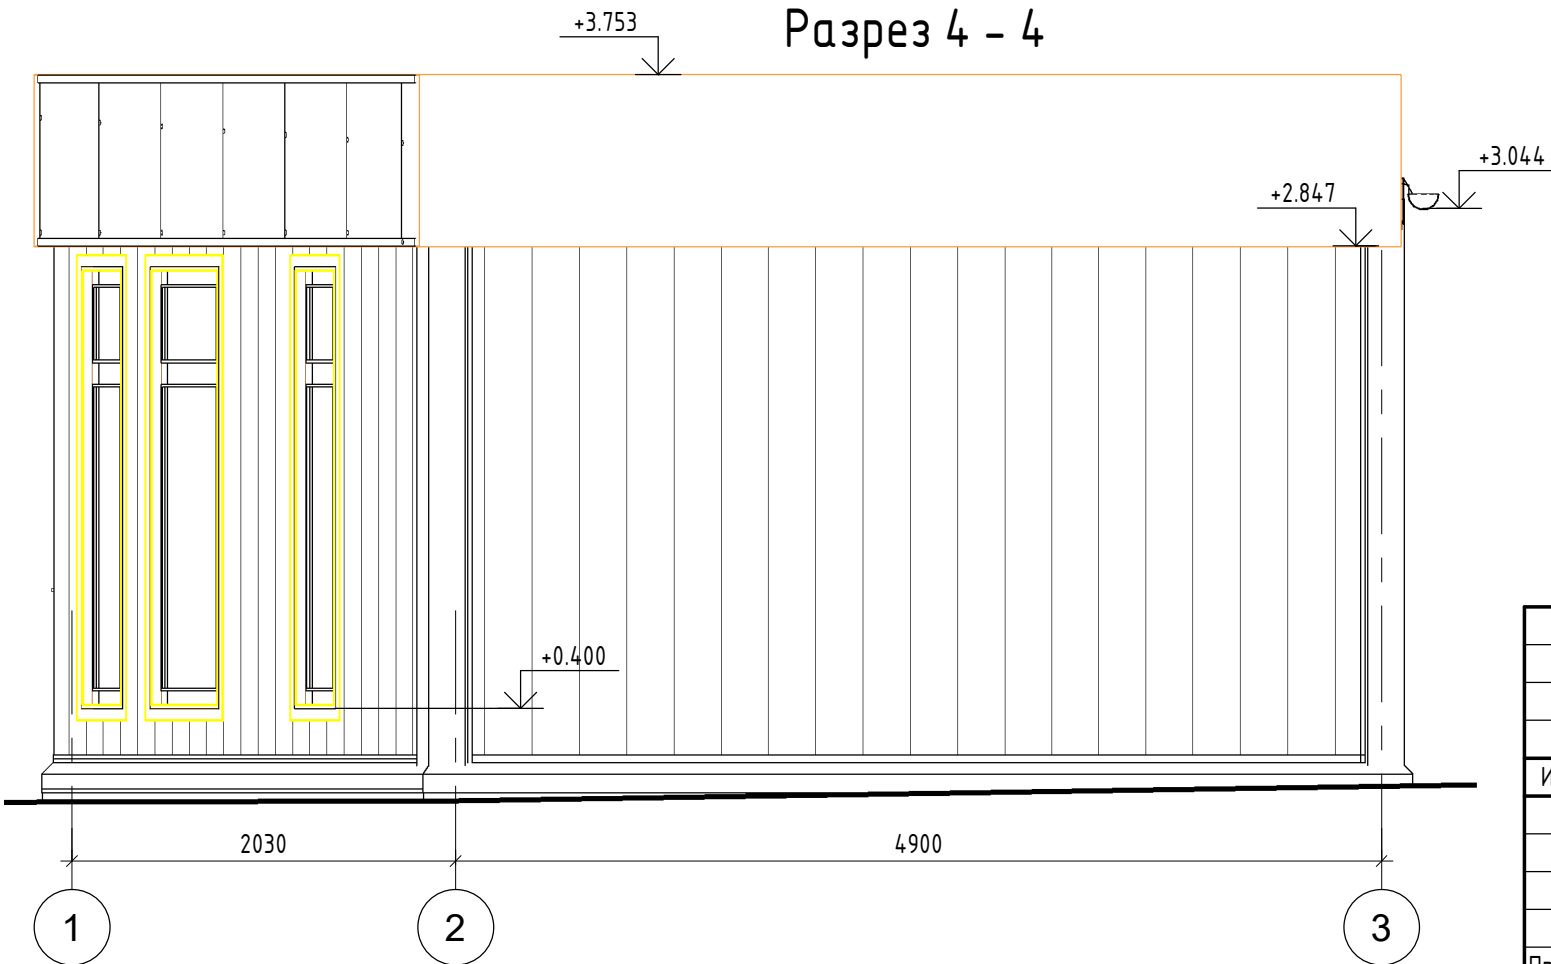


						809-25 - АР			
						Возведение объекта торгового назначения в районе ул. Речицкой и ул. Писателя Смирнова, 67 в г.Бресте			
Изм.	Кол.уч.	Лист	№ док.	Подп.	Дата				
						Павильон	Стадия	Лист	Листов
							П	3	
Проверил		Покалюк				Разрез 1-1,4-4			
Чертил		Ющенко							


Согласовано			
Инв. № подл.	Подп. и дата	Взам. инв. №	

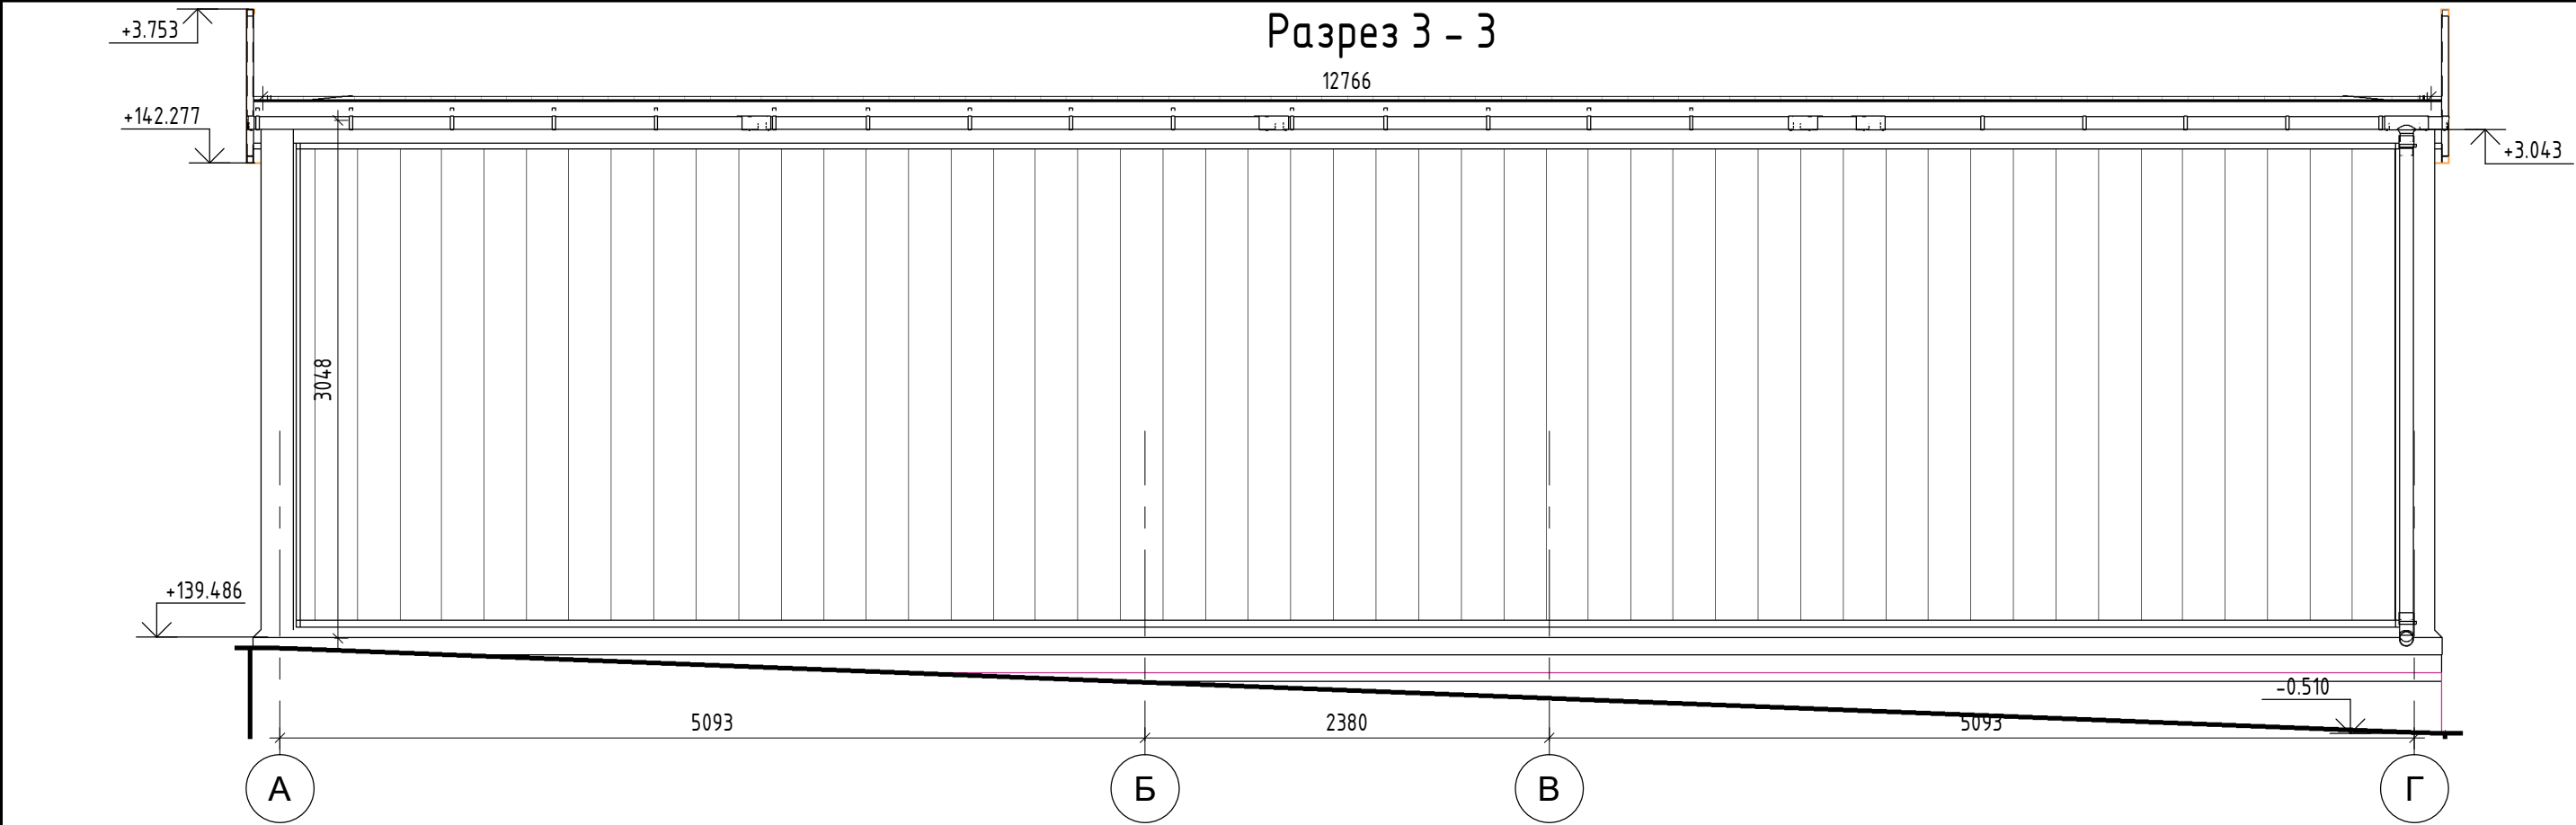

Разрез по задней части


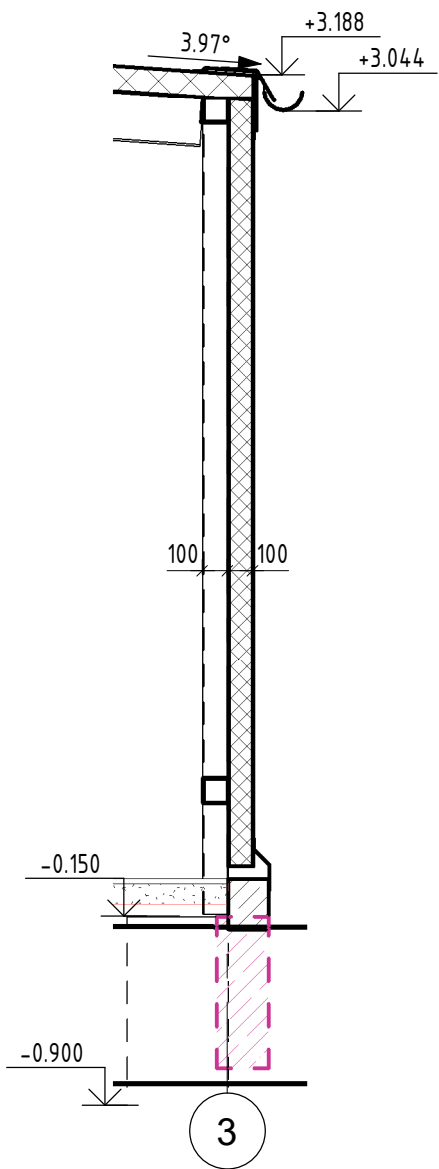


Разрез по фасадной части

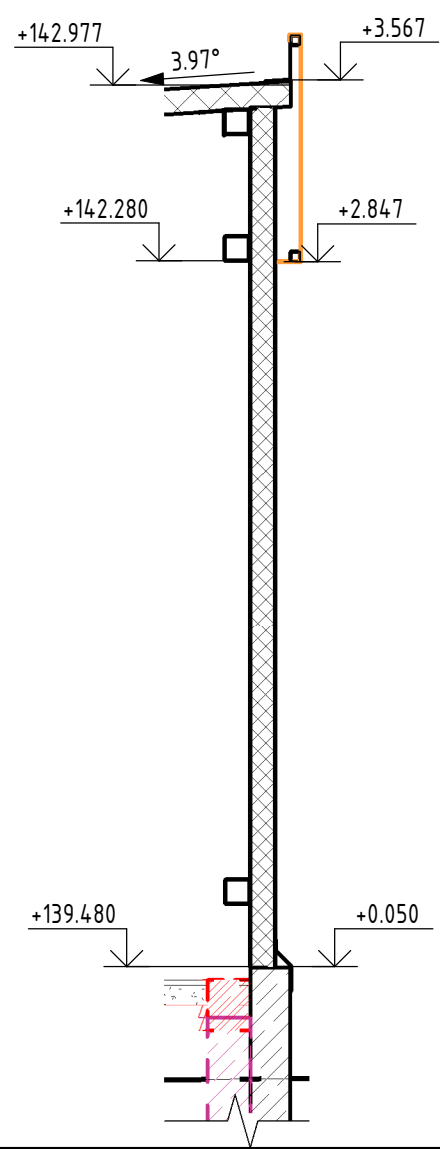

						809-25 - АР			
						Возведение объекта торгового назначения в районе ул. Речицкой и ул. Писателя Смирнова, 67 в г.Бресте			
Изм.	Кол.уч.	Лист	№ док.	Подп.	Дата	Павильон	Стадия	Лист	Листов
							П	4	
Проверил	Покалюк					Разрезы 3-3			
Чертил	Ющенко								


План крыши (1 : 50)

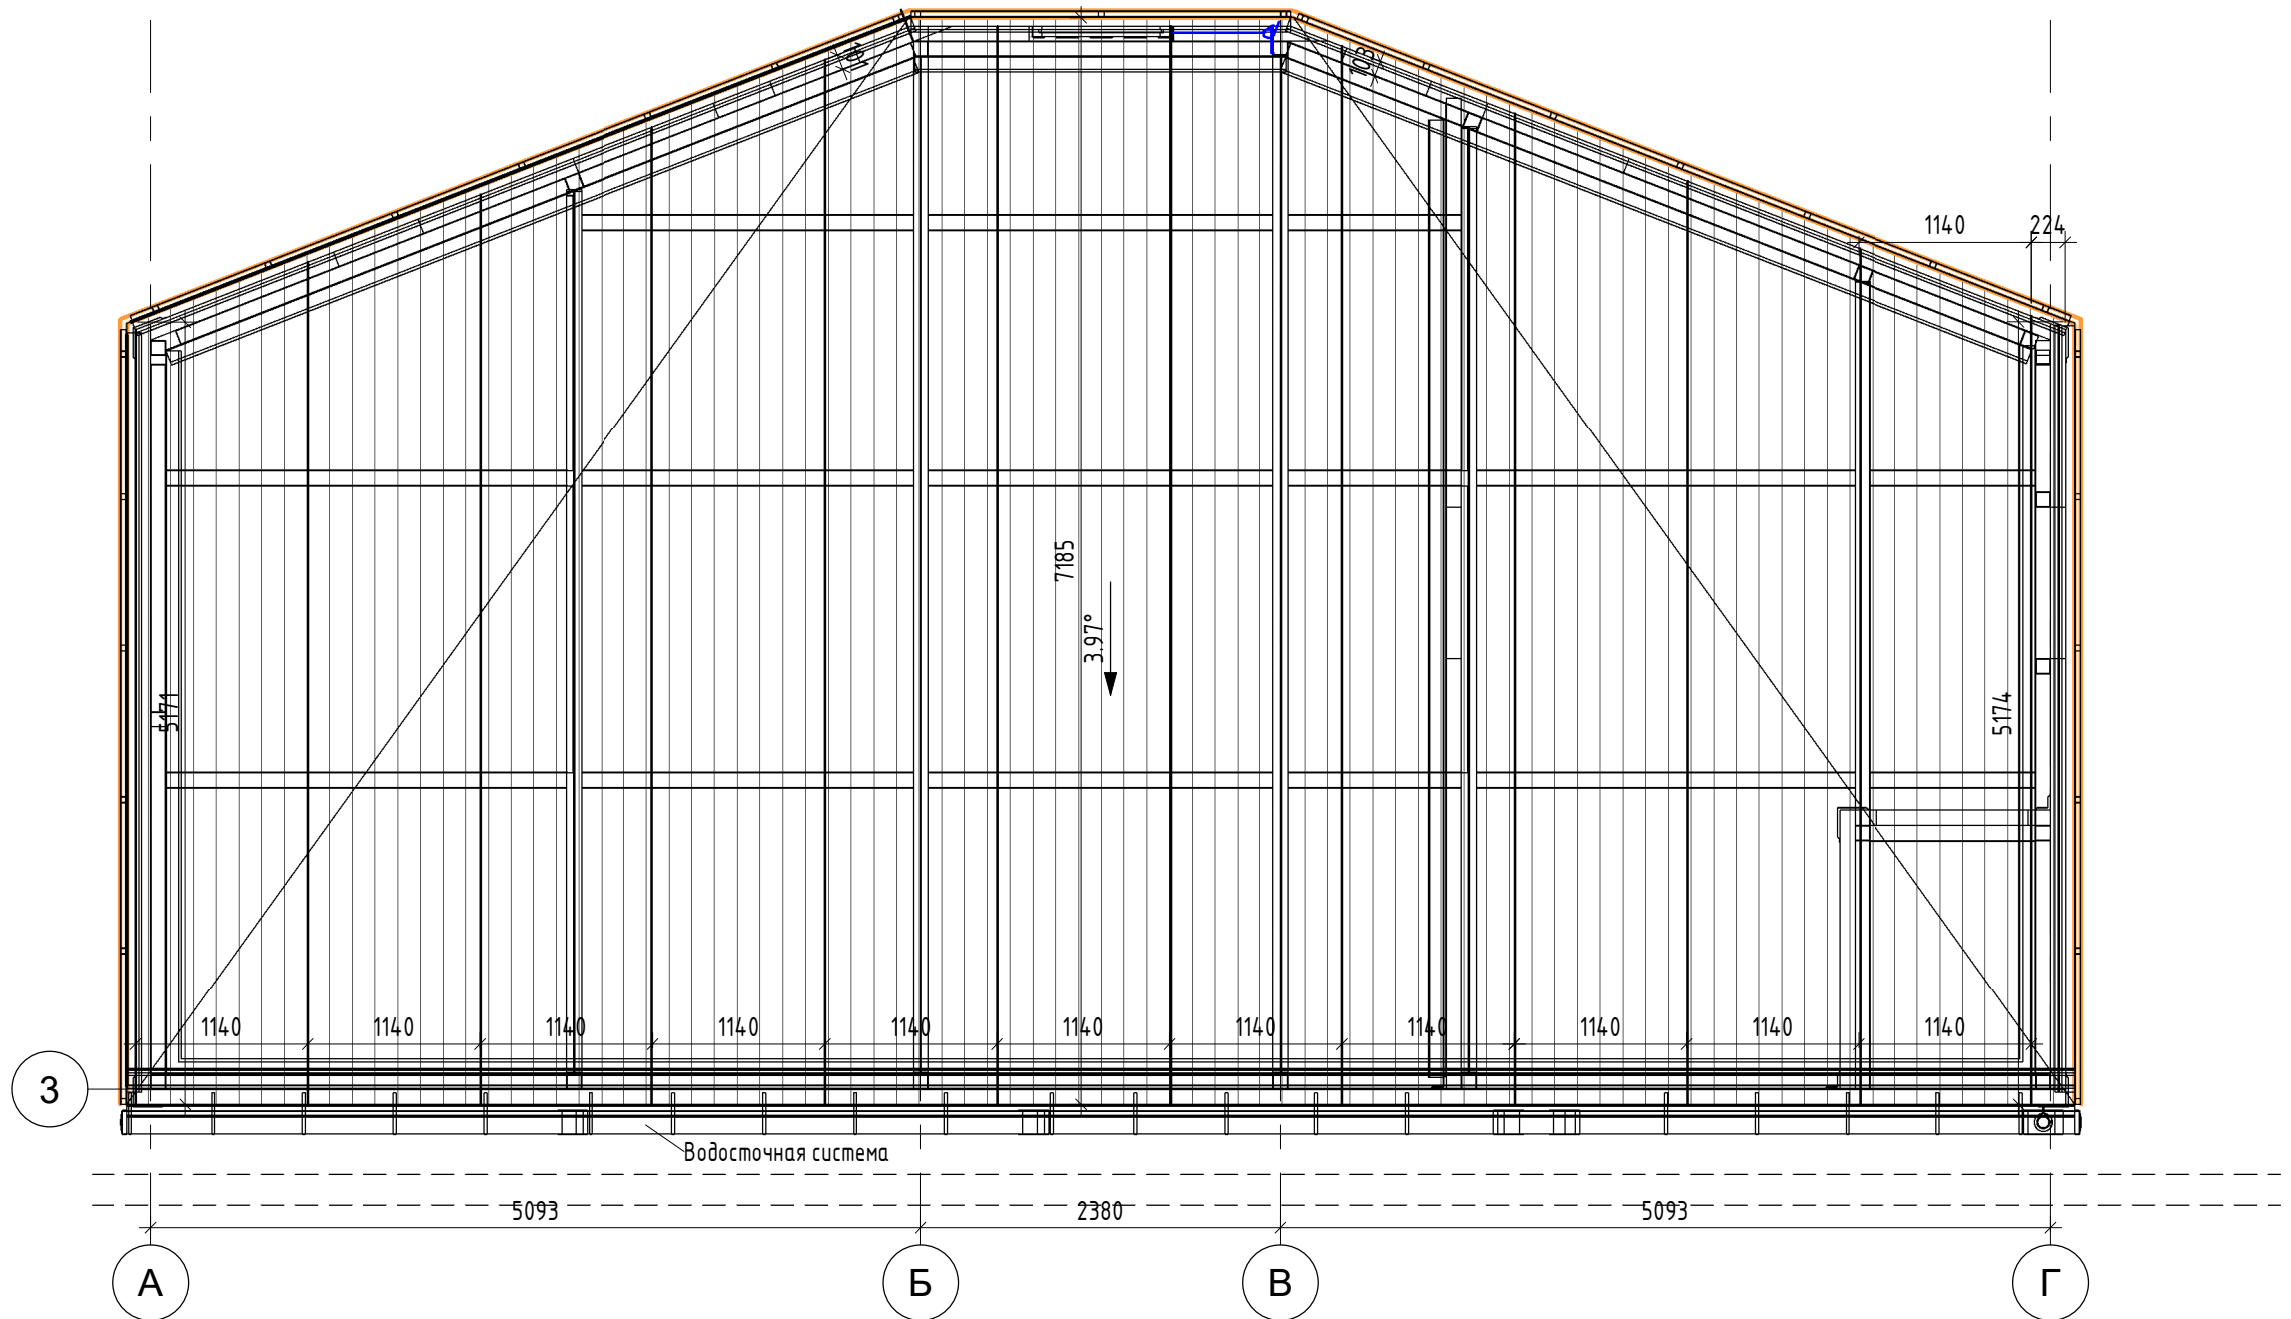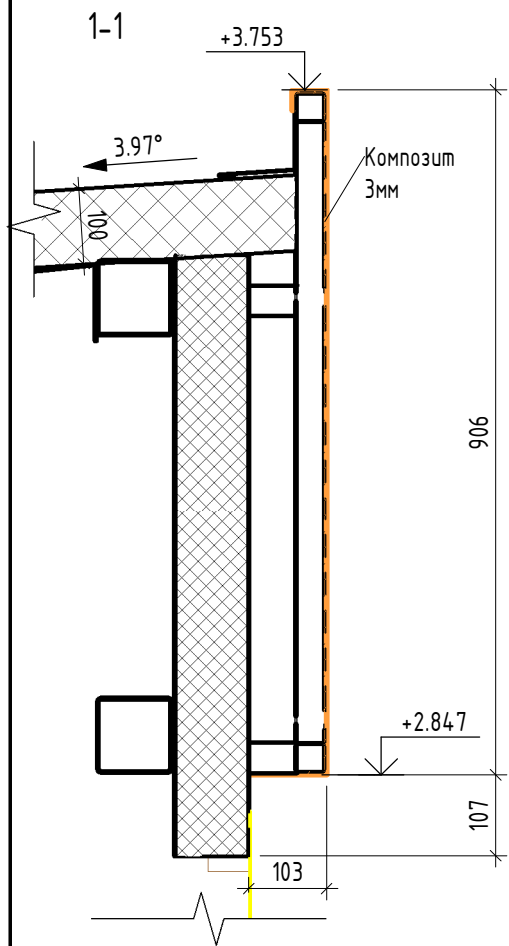

Инв. № подл.	Подп. и дата	Взам. инв. №	Согласовано			


						809-25 - АР			
						Возведение объекта торгового назначения в районе ул. Речицкой и ул. Писателя Смирнова, 67 в г.Бресте			
Изм.	Кол.уч.	Лист	№ док.	Подп.	Дата				
						Павильон	Стадия	Лист	Листов
							П	5	
Проверил		Покалюк				План крыши	 ALDENAGROUP		
Чертил		Ющенко							

Инв. № подл.	Подп. и дата	Взам. инв. №	Согласовано			

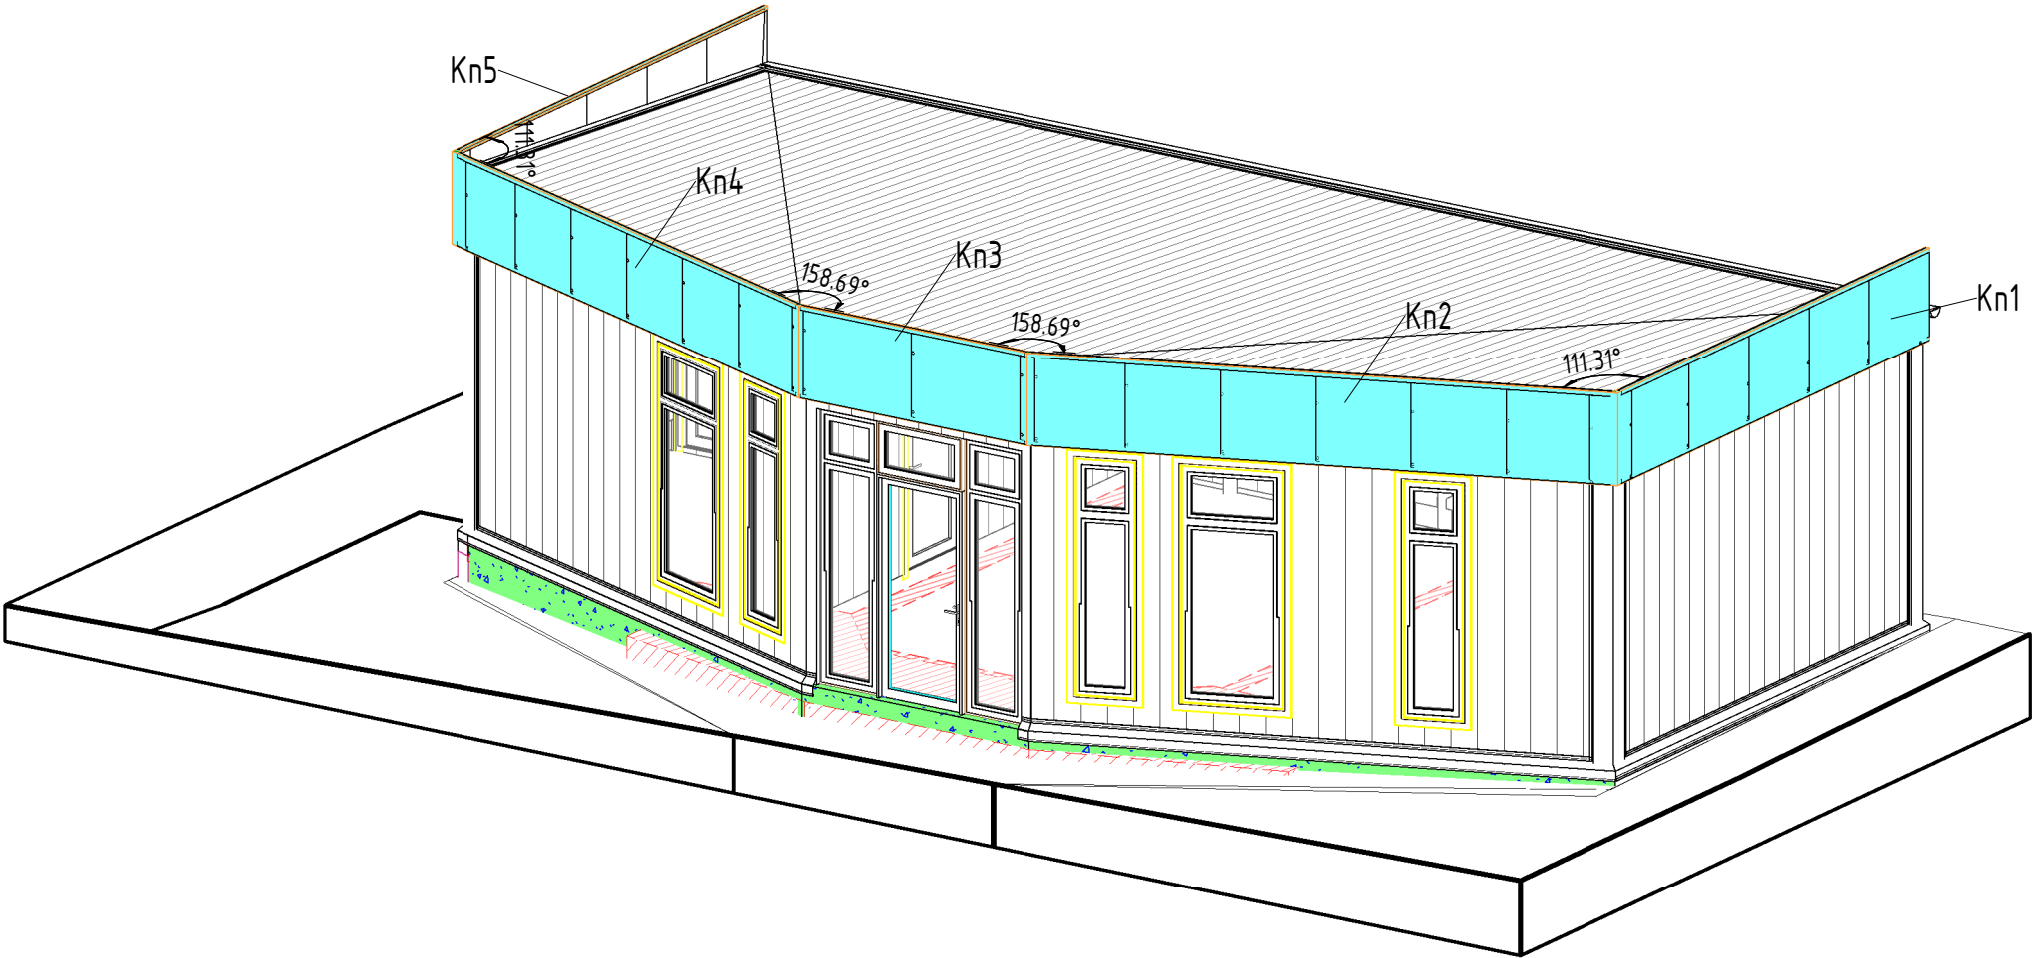

						809-25 - AP			
						Возведение объекта торгового назначения в районе ул. Речицкой и ул. Писателя Смирнова, 67 в г.Бресте			
Изм.	Кол.уч.	Лист	№ док.	Подп.	Дата	Павильон	Стадия	Лист	Листов
							П	18	
Проверил	Покалюк					Композит			
Чертил	Ющенко								

Вид

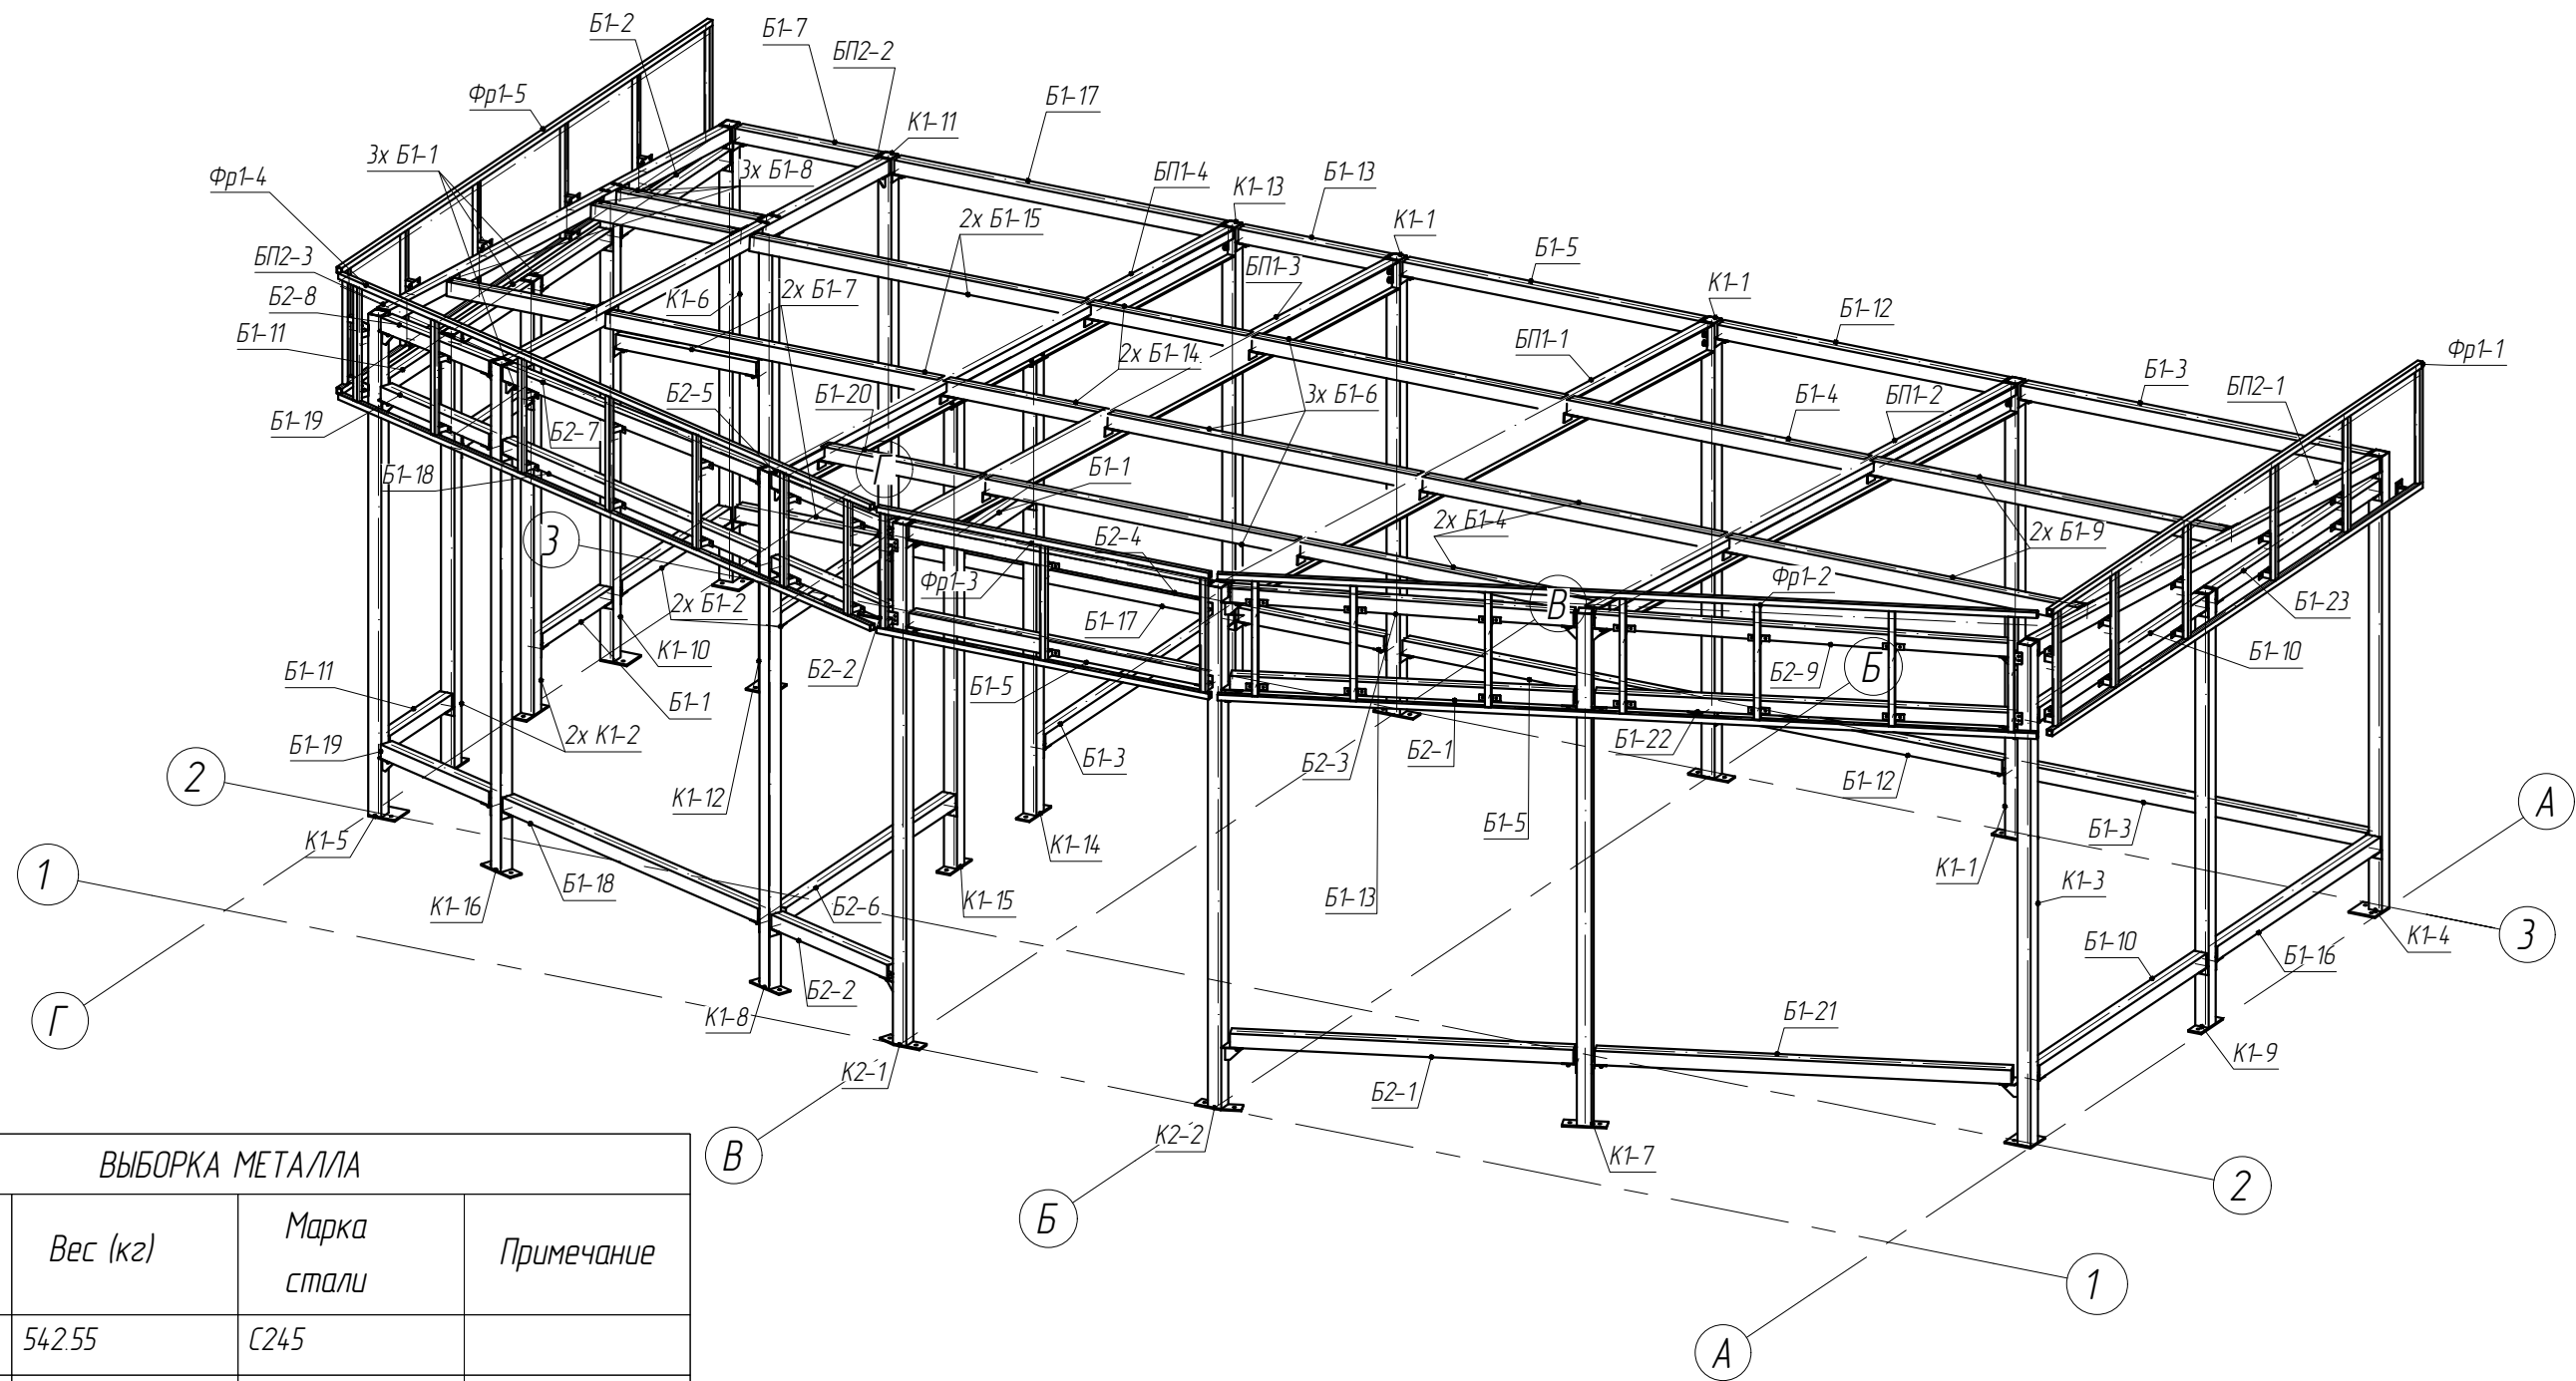

ВЫБОРКА МЕТАЛЛА

Профиль	Вес (кг)	Марка стали	Примечание
±20Б1	542.55	С245	
Л100х63х6	78.31	С245	
Л100х7	10.79	С245	
Л63х40х5	44.37	С245	
т 10	58.01	С245	
т 3	36.24	С245	
т 6	28.91	С245	
т 8	7.52	С245	
Гн. 40х2	171.99	С245	
Гн. 100х3	1793.32	С245	
На сварные швы:		27.72	
Итого:	2799.73		

						809-25			
						3д Вид. Ведомость металла	Стадия	Масса	Масштаб
									1:50
							Лист 54	Листов	
Изм.	Кол.уч	Лист	Ндок.	Подпись	Дата	Возведение объекта торгового назначения в г.Бресте по адресу ул. Смирнова 67А	ООО "АльденаГрупп"		
Гл.Инженер	Михнюк			05.06.2025					
				05.06.2025					
				05.06.2025					
На ч.произв.				05.06.2025					
Проверил	Покалюк			05.06.2025					
Констр.	Ющенко			05.06.2025					

Взам. инв. N

Подпись и дата

Инв. N подл.

Изм.	Кол.уч	Лист	Ндок.	Подпись	Дата
Гл.Инженер	Михнюк				05.06.2025
					05.06.2025
					05.06.2025
Нач.произв.					05.06.2025
Проверил	Покалюк				05.06.2025
Констр.	Ющенко				05.06.2025