

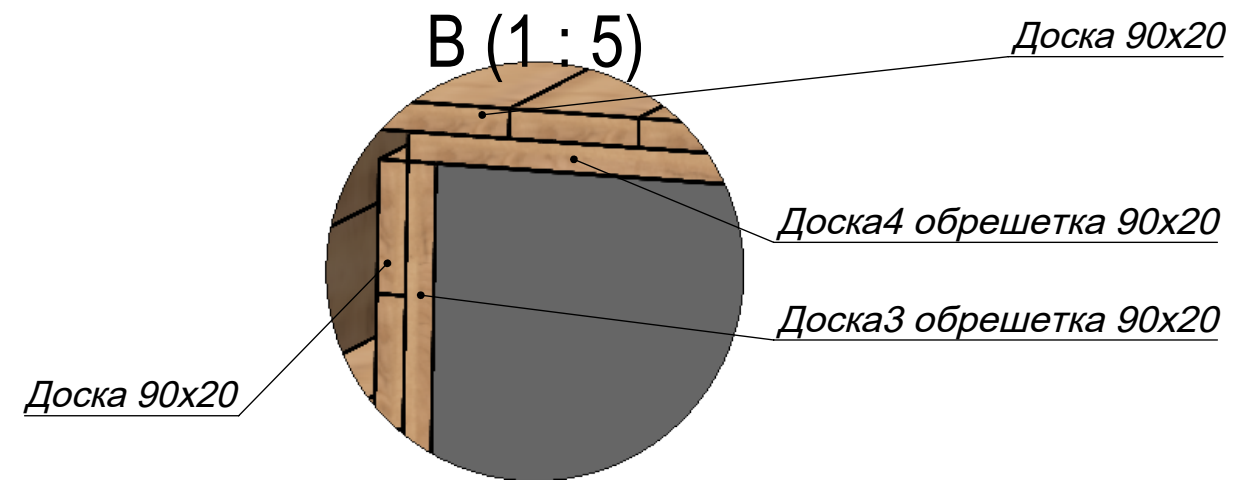
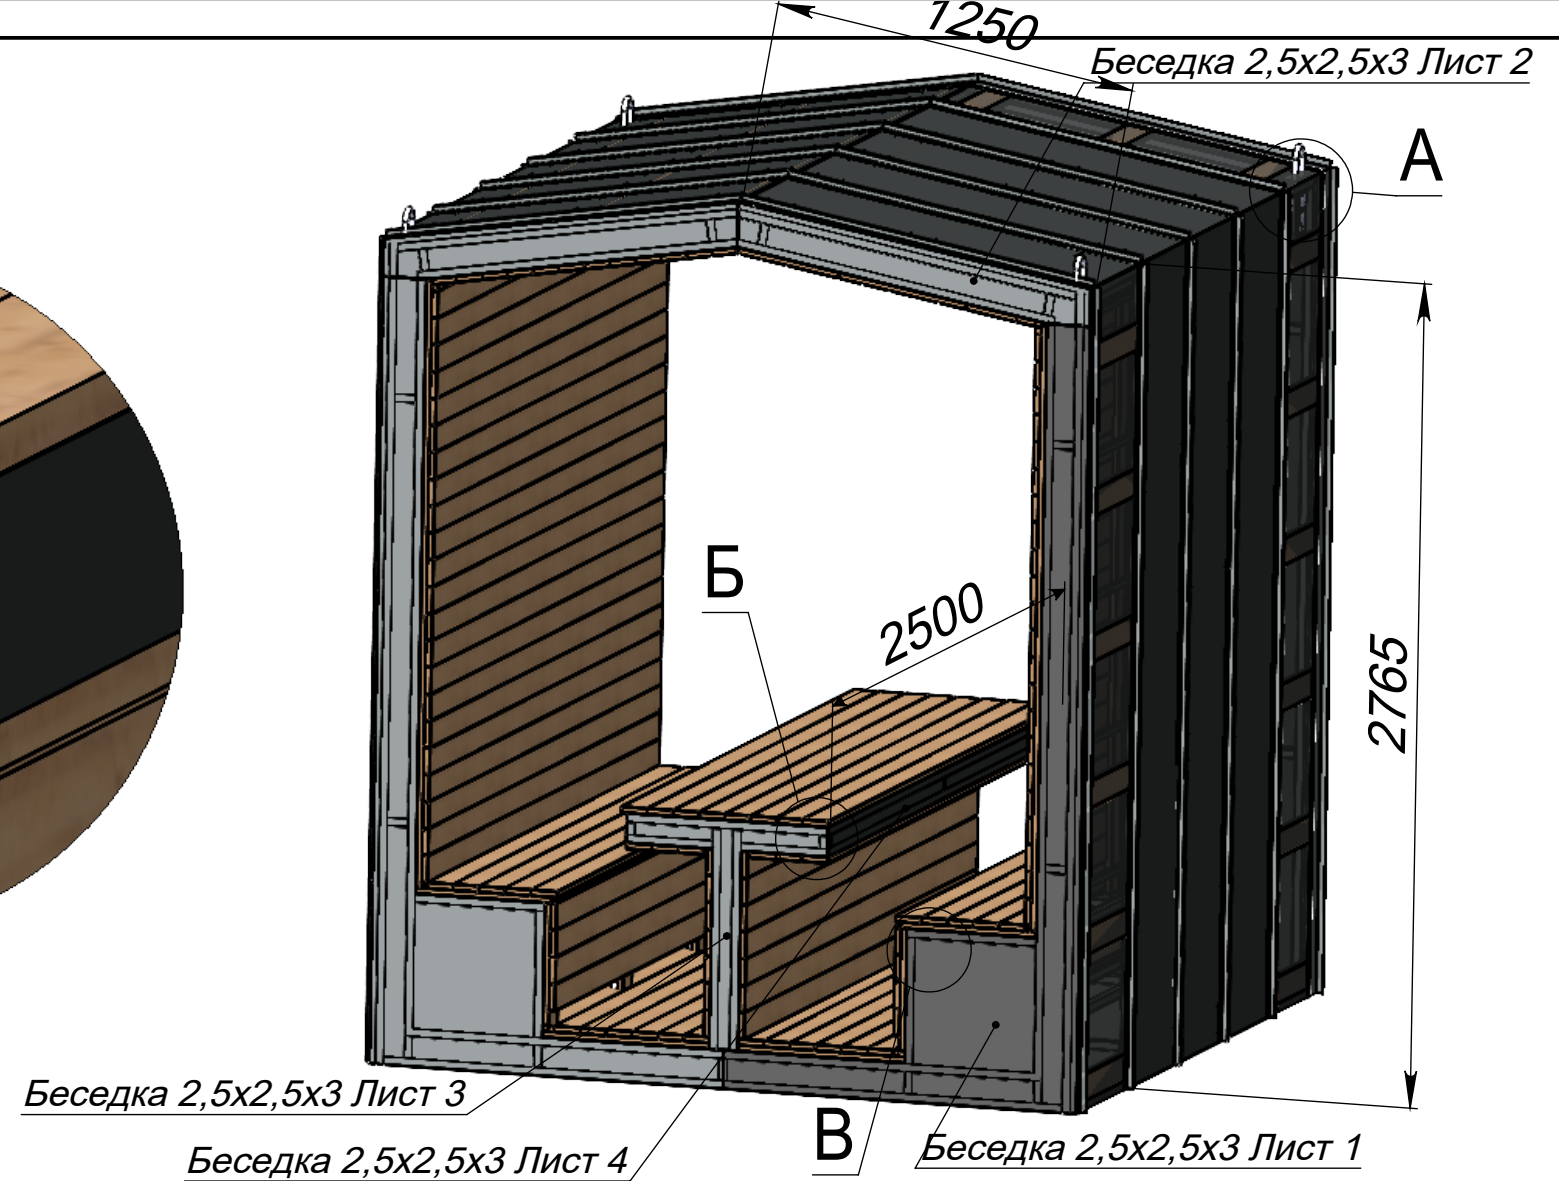
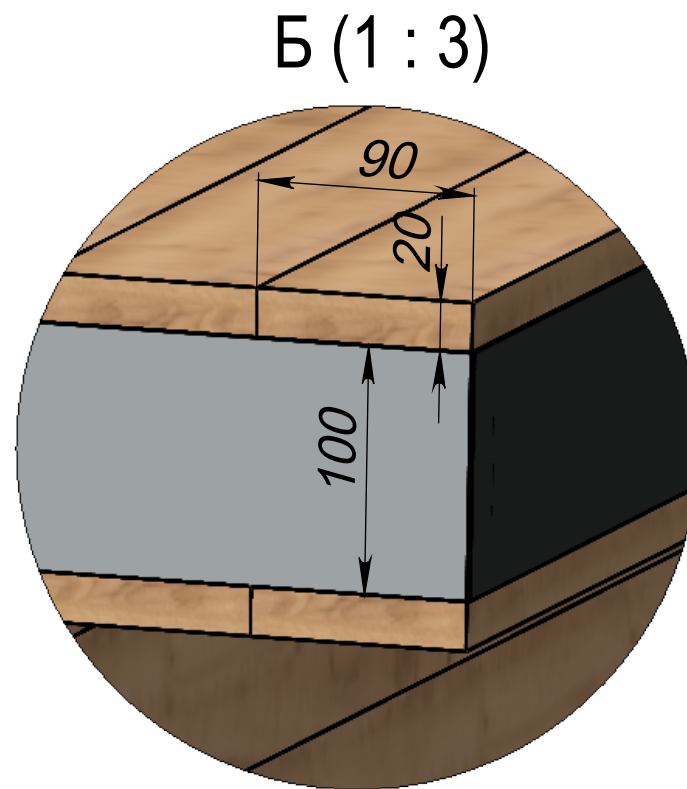


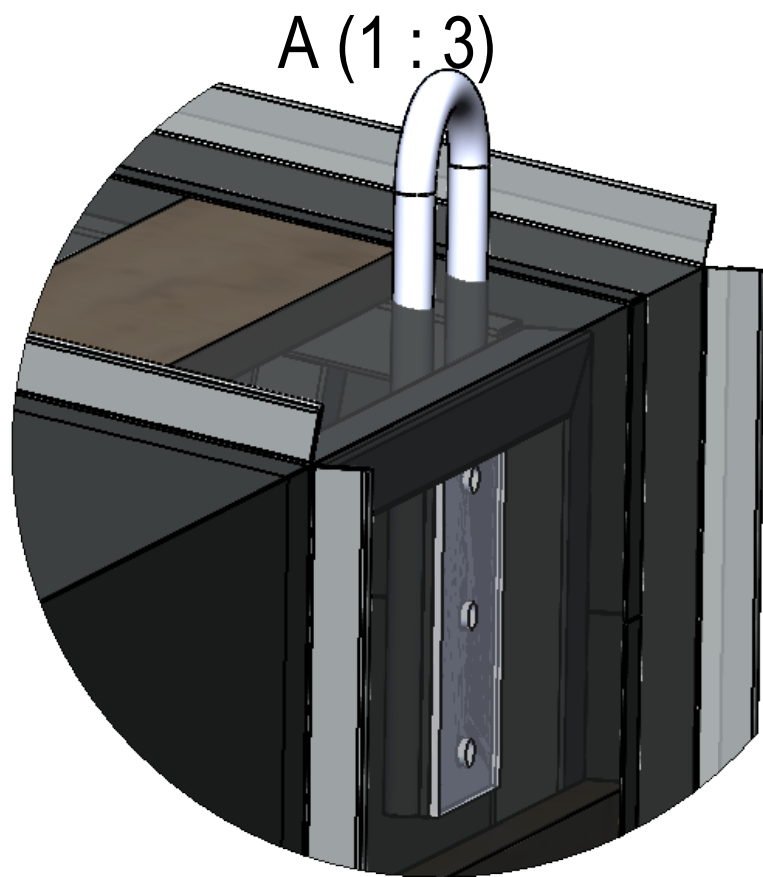

Кликфальц для кровли (L=0,8м-9м) esomaterial.by

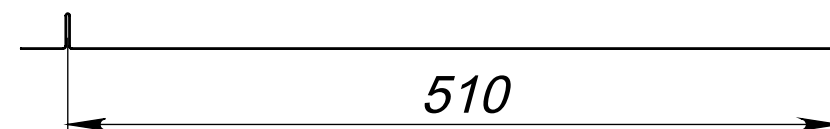

ПОЗИЦИЯ	ОБОЗНАЧЕНИЕ	ОПИСАНИЕ	К-ВО
1	Беседка 2,5х2,5х3 Каркас		2
2	Беседка 2,5х2,5х3 Лист 1		2
3	Беседка 2,5х2,5х3 Лист 2		2
4	Зеркально отразить Беседка 2,5х2,5х3 Лист 2		2
5	Зеркально отразить Беседка 2500х2500х3000 Лист 1		2
6	Доска 90х20	2500	130
7	Беседка 2,5х2,5х3 Лист 3	без загибов	2
8	Беседка 2,5х2,5х3 Лист 4	без загибов	2
9	МП 00.01 Пластина		8
10	МП 00.02 Петля		4
11	Доска1 обрешетка 90х20		18
12	Доска2 обрешетка 90х20		8
13	Доска3 обрешетка 90х20		8
14	Доска4 обрешетка 90х20		8
15	Доска5 обрешетка 90х20		8
16	Доска6 обрешетка 90х20		8
17	Кликфальц стены	2765	10
18	Кликфальц крыша	1250	10

Изм.	Лист	№ докум.	Подп.	Дата	Лист
					3