




Велопарковка Вп1

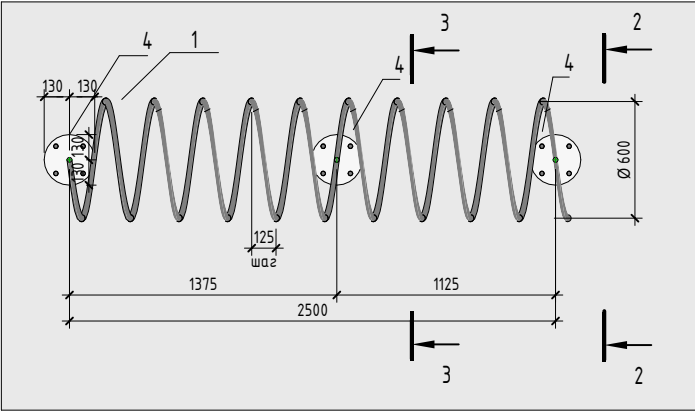


Разрез 1 - 1 (1 : 25)

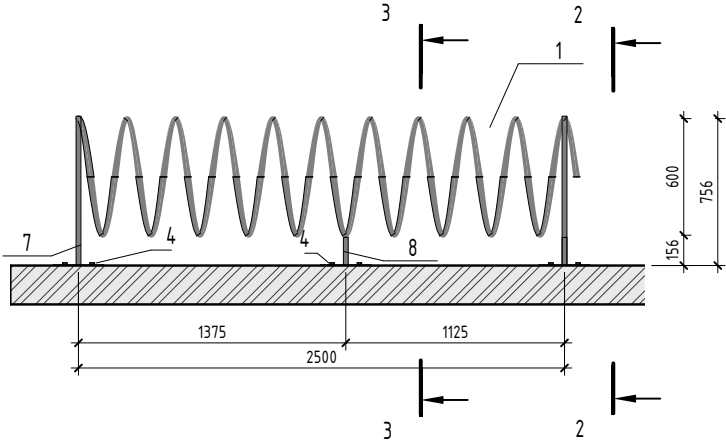


Разрез 2 - 2 (1 : 25)

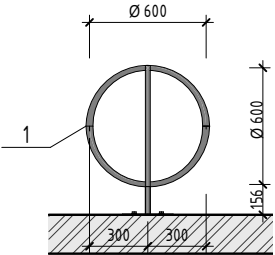

Разрез 3 - 3 (1 : 25)

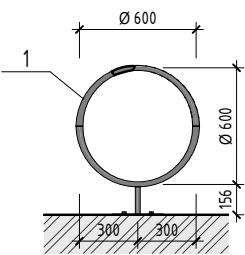

Марка.	Поз.	Наименование	Длина	Кол.	Масса, ед	Масса общ.
Вп1	1	Тр.нерж. $\dot{Y}25 \times 1,5$	20000	1	17,23	17,23
	4	-4x140	140	3	0,62	1,86
	7	Тр.нерж. $\dot{Y}25 \times 1,5$	766	2	0,66	1,32
	8	Тр.нерж. $\dot{Y}25 \times 1,5$	141	1	0,12	0,12
						20,53

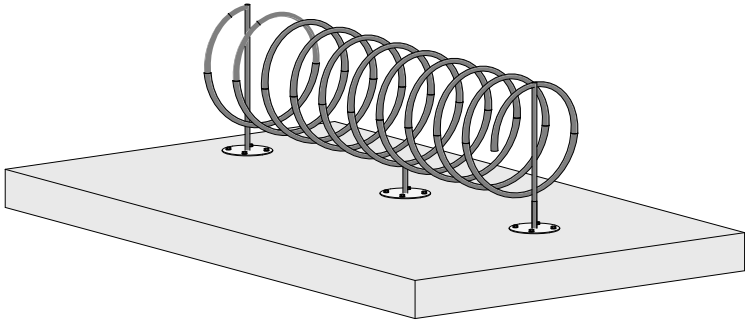

Крепление к тротуарной плитке на химический анкер (шпилька М10)
в заранее пробуренное отверстие $\dot{Y}12$ мм.
Расход метизов:
Шпилька М10 - 2м
Шайба М10 - 12шт
Гайка колпачковая М10 - 12шт
Хим. анкер 300ml - 1 баллон

						883-26 - КР			
						Велопарковка спираль			
Изм.	Кол.уч.	Лист	№ док.	Подп.	Дата	Велопарковка.	Стадия	Лист	Листов
Разработал	Покалюк Д.Г.						КР	02	
Проверил	Покалюк Д.Г.					Велопарковка Вп1	ООО "АльденаГрупп"		