


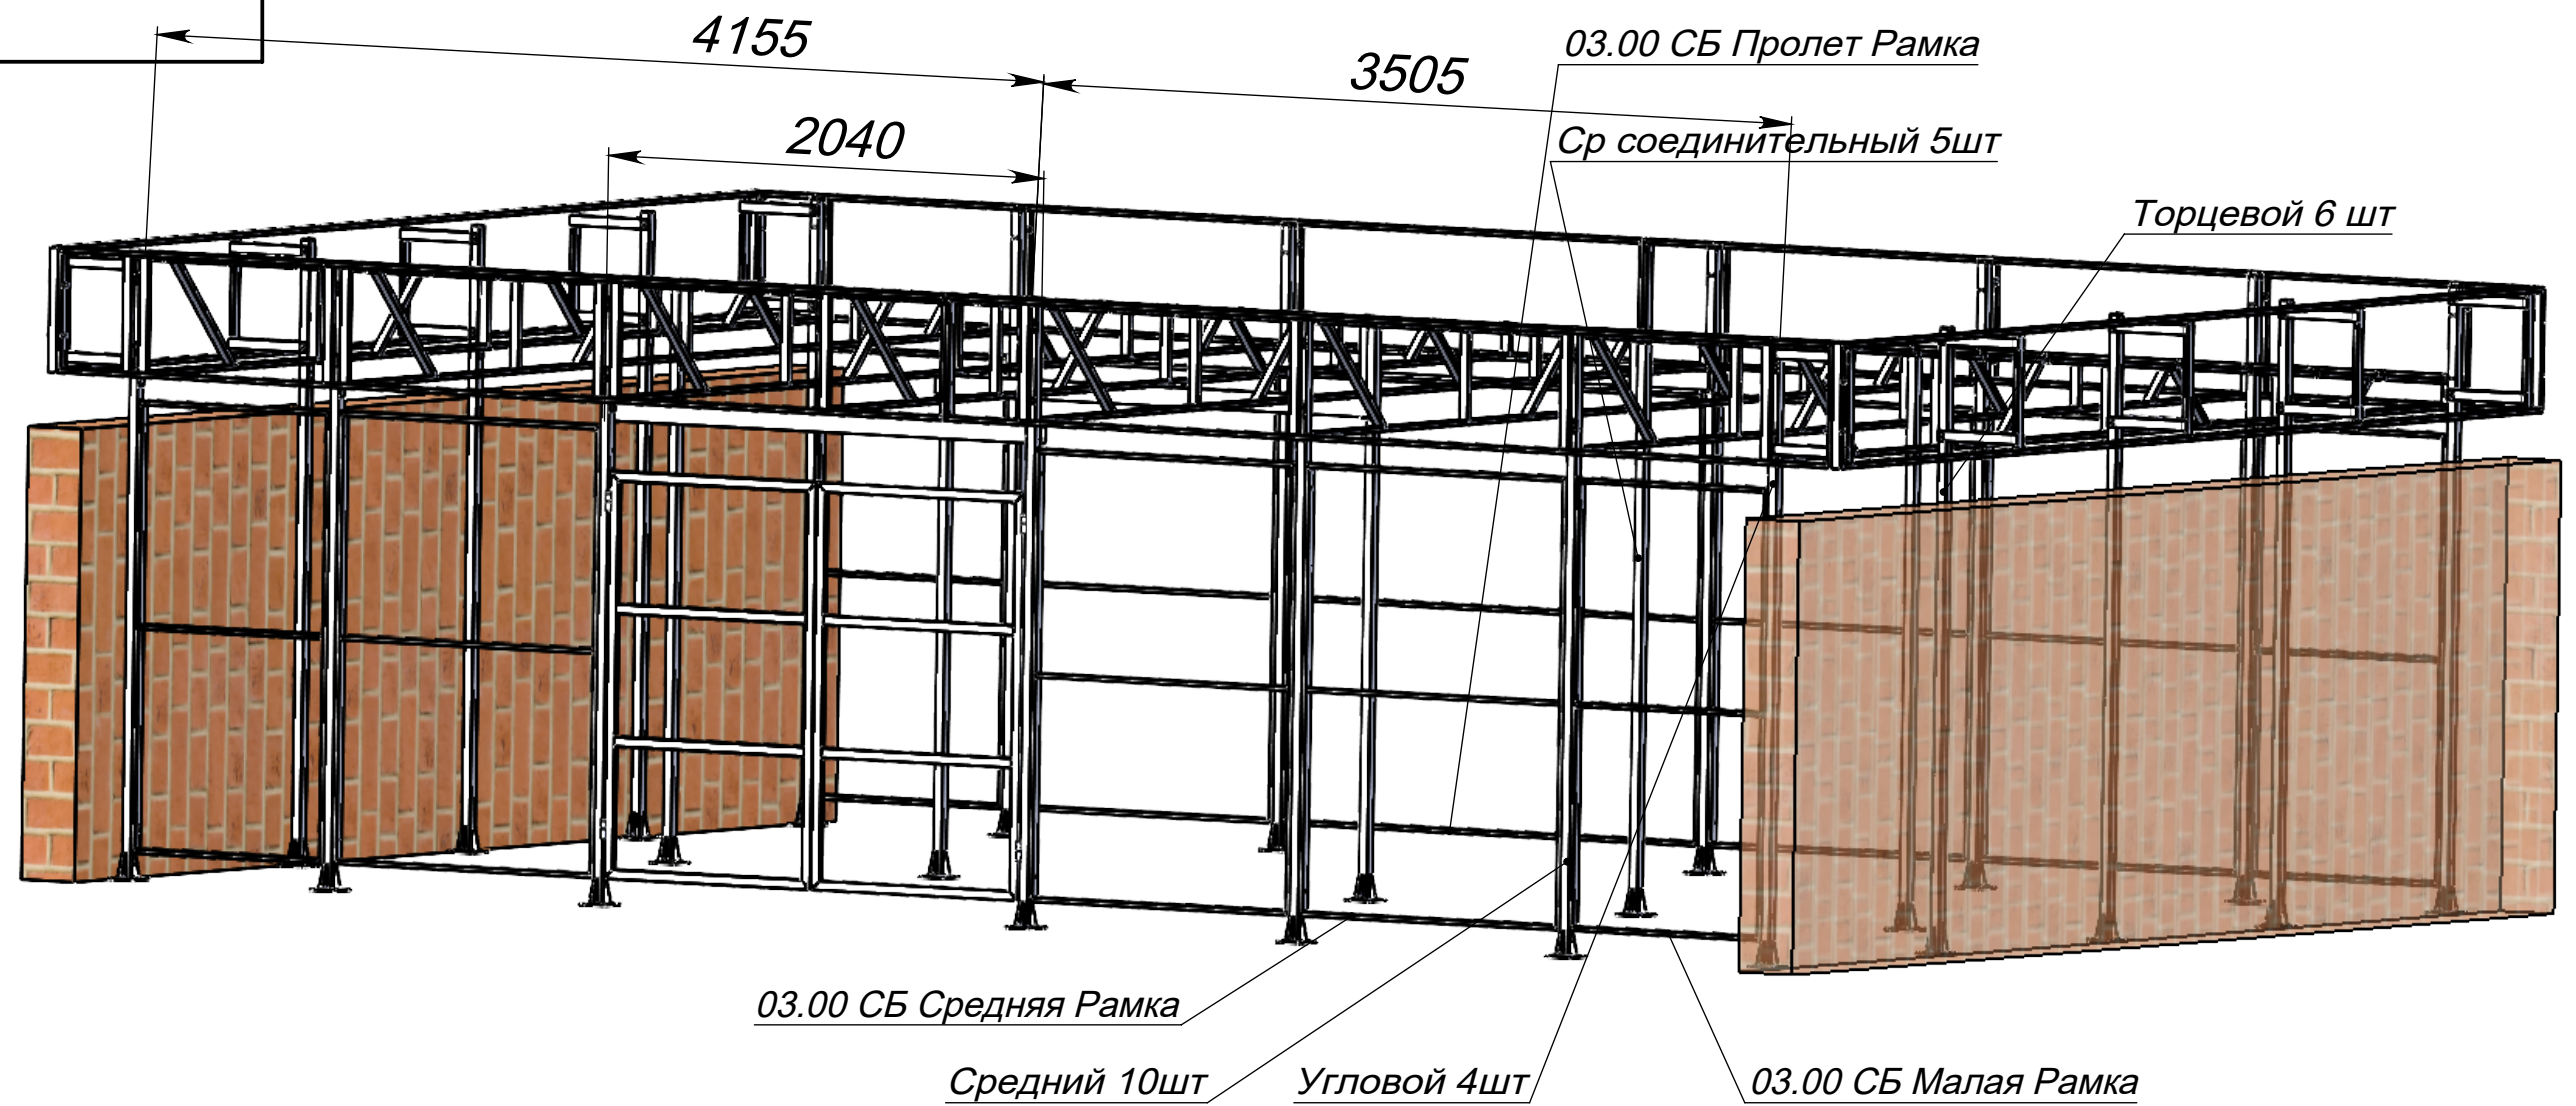

ПОЗИЦИЯ	ОБОЗНАЧЕНИЕ	ОПИСАНИЕ	К-ВО
1	Фундамент под Н 8.3х5.7х2.5		1
2	Н 8.3х5.7х2.5 01.00 СБ Столб	Угловой	4
3	Н 8.3х5.7х2.5 01.00 СБ Столб	Торцевые	6
4	Н 8.3х5.7х2.5 01.00 СБ Столб	Средний	10
5	Н 8.3х5.7х2.5 01.00 СБ Столб	Ср соединительный	5
6	Н 8.3х5.7х2.5 03.00 СБ Рамка	Малая	4
7	Н 8.3х5.7х2.5 03.00 СБ Рамка	Средняя	6
8	Н 8.3х5.7х2.5 03.00 СБ Рамка	Пролет	1
9	Н 8.3х5.7х2.5 05.00 СБ Ферма		8
10	40х20 Обрешетка1	L=3505	11
11	40х20 Обрешетка2	L=4155	11
12	Н 8.3х5.7х2.5 07.00 СБ Рамка		2
13	Н 8.3х5.7х2.5 09.00 Дверь СБ		1
14	Петля цилиндр ф16		4
15	Зеркально отразитьН 8.3х5.7х2.5 09.00 Дверь СБ		1
16	Н 8.3х5.7х2.5 08.00 СБ Рамка		2
17	Н 8.3х5.7х2.5 00.03 Стена		2
18	Н 8.3х5.7х2.5 09.00 СБ Рамка		2
19	80х40 Перемычка	2040	3

Изм.	Лист	№ докум.	Подп.	Дата	Лист
					1